Provinsi : Sumatera Utara

Kabupaten : Labuhanbatu

Lampiran D.I 201.C

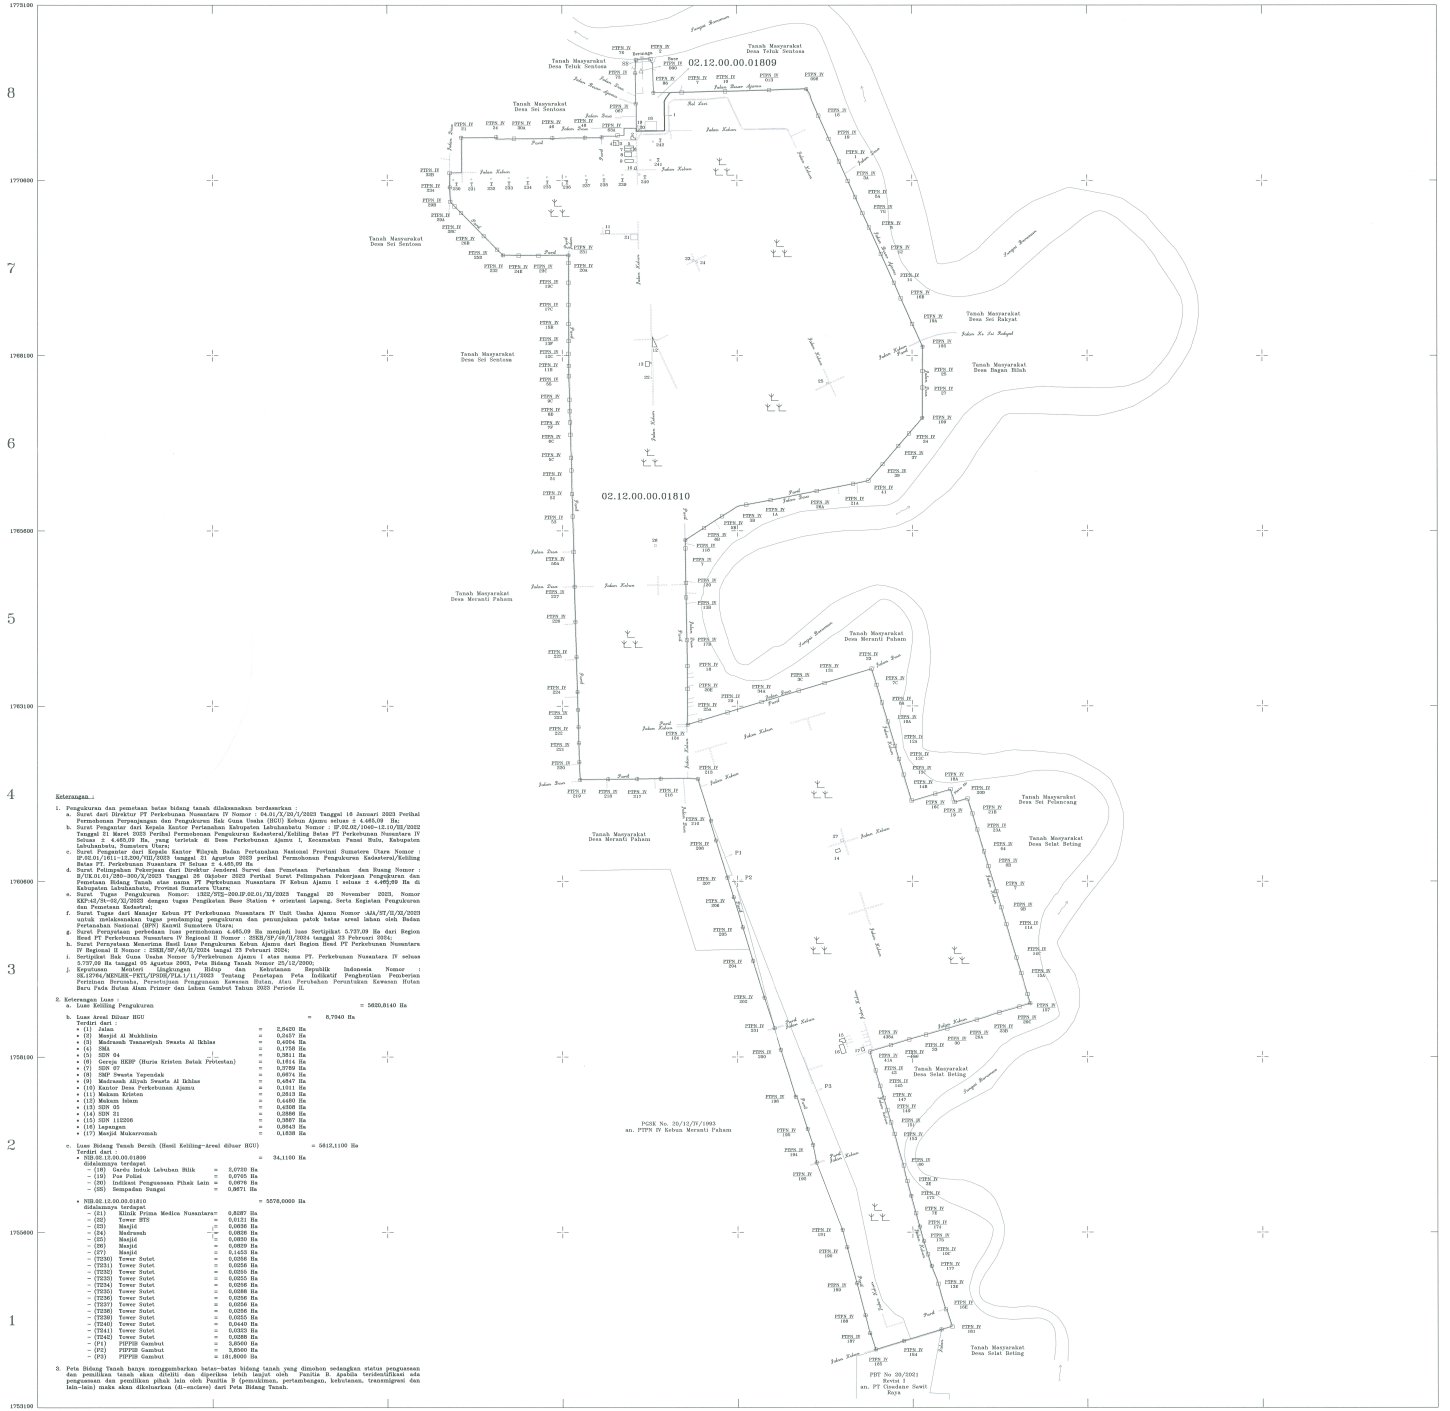

Keterangan :

1. Pengukuran dan pemetaan batas bidang tanah dilaksanakan berdasarkan :
   a. Surat dari Direktur PT Perkebunan Nusantara IV Nomor : 04.01/X/20/1/2023 Tanggal 16 Januari 2023 Perihal Permohonan Pengukuran dan Pengukuran Hak Guna Usaha (HGU) Kebun Ajamu seluas ± 4.465,09 Ha;
   b. Surat Pengantar dari Kepala Kantor Pertanahan Kabupaten Labuhanbatu Nomor : IP.02.02/1040-12.10/III/2022 Tanggal 21 Maret 2023 Perihal Permohonan Pengukuran Kadastral/Keliling Batas PT Perkebunan Nusantara IV Seluas ± 4.465,09 Ha, yang terletak di Desa Perkebunan Ajamu I, Kecamatan Panai Hulu, Kabupaten Labuhanbatu, Sumatera Utara;
   c. Surat Pengantar dari Kepala Kantor Wilayah Badan Pertanahan Nasional Provinsi Sumatera Utara Nomor : 1.02.01.01/IP-300/X/2023 Tanggal 26 Oktober 2023 Perihal Permohonan Pengukuran Kadastral/Keliling Batas PT. Perkebunan Nusantara IV Seluas ± 4.465,09 Ha
   d. Surat Pelimpahan Pekerjaan dari Direktur Jenderal Survei dan Pemetaan Pertanahan dan Ruang Nomor : B/13L.01.01/IBD-300/X/2023 Tanggal 26 Oktober 2023 Perihal Surat Pelimpahan Pekerjaan Pengukuran dan Pemetaan Bidang Tanah atas nama PT Perkebunan Nusantara IV Kebun Ajamu I seluas ± 4.465,09 Ha di Kabupaten Labuhanbatu, Provinsi Sumatera Utara;
   e. Surat Tugas Pengukuran Nomor: 1322/ST2-200.IP.02.01/XI/2023 Tanggal 20 November 2023, Nomor ST-42/24-02/XI/2023 dengan tugas Pengikatan Base Station & orientasi lapang, Serta Kegiatan Pengukuran dan Pemetaan Bidang Tanah;
   f. Surat Tugas dari Manajer Kebun PT Perkebunan Nusantara IV Unit Usaha Ajamu Nomor :AAA/ST/II/XI/2023 untuk melaksanakan tugas pendampingan pengukuran dan penunjukan patok batas areal lahan oleh Badan Pertanahan Nasional (BPN) Kawali Sumatera Utara;
   g. Surat Persyetaan perbedaan luas permohonan 4.465,09 Ha menjadi luas Sertifikat 5.737,09 Ha dari Region Head PT Perkebunan Nusantara IV Regional II Nomor : SSKB/SP/48/II/2024 tanggal 23 Februari 2024;
   h. Surat Persyetaan Monotina Hasil Luas Pengukuran Kebun Ajamu dari Region Head PT Perkebunan Nusantara IV Regional II Nomor : SSKB/SP/48/II/2024 tanggal 23 Februari 2024;
   i. Sertipikat Hak Guna Usaha Nomor 1/Perkebunan Ajamu I atas nama PT. Perkebunan Nusantara IV seluas 5.737,09 Ha tanggal 03 Agustus 2003, Peta Bidang Tanah Nomor 25/12/2003;
   j. Surat Keputusan Menteri Agraria dan Tata Ruang/Kepala Badan Pertanahan Republik Indonesia Nomor : SK.13766/MENLHK-PKTL/IPSDH/PLA.1/11/2023 Tentang Penetapan Peta Indikatif Penghentian Pemberian Pertimbangan Teknis Pelepasan Kawasan Hutan, Perubahan Peruntukan Kawasan Hutan dan Perubahan Fungsi Kawasan Hutan Produksi Yang Dapat Dikonversi Seluas 1.000 (seribu) Hektar di Provinsi Sumatera Utara, Provinsi Riau, Provinsi Kepulauan Riau, Provinsi Jambi, Provinsi Sumatera Selatan, Provinsi Bangka Belitung, Provinsi Bengkulu, Provinsi Lampung, Provinsi Banten, Provinsi Jawa Barat, Provinsi Jawa Tengah, Provinsi Jawa Timur, Provinsi Kalimantan Barat, Provinsi Kalimantan Tengah, Provinsi Kalimantan Selatan, Provinsi Kalimantan Timur, Provinsi Kalimantan Utara, Provinsi Sulawesi Utara, Provinsi Sulawesi Tengah, Provinsi Sulawesi Selatan, Provinsi Sulawesi Tenggara, Provinsi Gorontalo, Provinsi Sulawesi Barat, Provinsi Maluku, Provinsi Maluku Utara, Provinsi Papua, Provinsi Papua Barat, Provinsi Papua Selatan, Provinsi Papua Tengah, Provinsi Papua Pegunungan, Provinsi Papua Barat Daya Untuk Kepentingan Pembangunan Perkebunan Kelapa Sawit, Tebu, Dan Tanaman Pangan Atas Nama Perusahaan Perkebunan Negara, Perusahaan Perkebunan Swasta, Koperasi, Dan Perseorangan Tahun 2023 Tanggal 16 Januari 2023 Perihal Permohonan Pengukuran dan Pengukuran Hak Guna Usaha (HGU) Kebun Ajamu seluas ± 4.465,09 Ha;

2. Keterangan Luas :
   a. Luas Kelilling Pengukuran = 5620,8140 Ha
   b. Luas Areal Dibuar HGU = 8,7940 Ha
      Terdiri dari :
      - (1) Jalan = 2,8420 Ha
      - (2) Masjid Al Mukhlisin = 0,2457 Ha
      - (3) Madrasah Tsanawiyah Swasta Al Ikhlas = 0,4084 Ha
      - (4) SMA = 0,1758 Ha
      - (5) SDN 04 = 0,2811 Ha
      - (6) Gereja HKBP (Huria Kristen Batak Protestan) = 0,1916 Ha
      - (7) SDN 05 = 0,3894 Ha
      - (8) SMP Swasta Yapendah = 0,9974 Ha
      - (9) Madrasah Aliyah Swasta Al Ikhlas = 0,4847 Ha
      - (10) Kantor Desa Perkebunan Ajamu = 0,1011 Ha
      - (11) Makam Kristen = 0,2813 Ha
      - (12) Makam Islam = 0,4480 Ha
      - (13) SDN 05 = 0,4308 Ha
      - (14) SDN 21 = 0,2886 Ha
      - (15) SDN 112206 = 0,3867 Ha
      - (16) Lapangan = 0,8643 Ha
      - (17) Masjid Mukarromah = 0,1838 Ha
   c. Luas Bidang Tanah Bersih (Hasil Kelilling-Areal dibuar HGU) = 5612,1100 Ha
      Terdiri dari :
      - 9SB.BC.12.00.01809 = 34,1100 Ha
        didalamnya terdapat :
        - (18) Garda Indok Lebuhan Bilik = 0,0720 Ha
        - (19) Pos Polisi = 0,0765 Ha
        - (20) Indikasi Penguasaan Pihak Lain = 0,0076 Ha
        - (SS) Sempadan Sungai = 0,0671 Ha
      - 9SB.BC.12.00.01810 = 5578,0000 Ha
        didalamnya terdapat :
        - (21) Klinik Prima Medica Nusantara= 0,0287 Ha
        - (22) Tower BTS = 0,0121 Ha
        - (23) Masjid = 0,0038 Ha
        - (24) Madrasah = 0,0026 Ha
        - (25) Masjid = 0,0030 Ha
        - (26) Masjid = 0,0039 Ha
        - (27) Masjid = 0,1453 Ha
        - (T230) Tower Sutet = 0,0256 Ha
        - (T231) Tower Sutet = 0,0256 Ha
        - (T232) Tower Sutet = 0,0255 Ha
        - (T233) Tower Sutet = 0,0255 Ha
        - (T234) Tower Sutet = 0,0256 Ha
        - (T235) Tower Sutet = 0,0256 Ha
        - (T236) Tower Sutet = 0,0256 Ha
        - (T237) Tower Sutet = 0,0256 Ha
        - (T238) Tower Sutet = 0,0256 Ha
        - (T239) Tower Sutet = 0,0255 Ha
        - (T240) Tower Sutet = 0,0440 Ha
        - (T241) Tower Sutet = 0,0323 Ha
        - (T242) Tower Sutet = 0,0288 Ha
        - (P1) PIPPIB Gambut = 5,6560 Ha
        - (P2) PIPPIB Gambut = 3,8560 Ha
        - (P3) PIPPIB Gambut = 181,6000 Ha

3. Peta Bidang Tanah hanya menggambarkan batas-batas bidang tanah yang dimohon sedangkan status penguasaan dan pemilikan tanah akan dijelliti dan diperiksa lebih lanjut oleh Panitia B. apabila teridentifikasi ada penguasaan dan pemilikan pihak lain oleh Panitia B (pemukiman, pertambangan, kehutanan, transmigrasi dan lain-lain) maka akan dikeluarkan (di-enclave) dari Peta Bidang Tanah.

PETA BIDANG TANAH
No. 4/2024

Skala 1 : 25.000

Kecamatan	Panai Hulu
Desa	Perkebunan Ajamu

PETUNJUK LETAK BIDANG TANAH
ZONE : 47.2

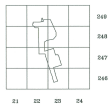

Keterangan

Peta ini dibuat berdasarkan pengukuran kelilling batas bidang tanah dengan pengamatan GNSS Geodetik GNCNAV (S) metode Real Time Kinematic, Statik dan Rapid Statik pada tugu-tugu batas bidang tanah dengan sistem koordinat TM3 Zona 47.2 dengan Koordinat Base Point X = 162351.1405 Y = 177315.0175 yang diikat ke Stasiun Cors BIG Kode (CKPU) Kota Pinang dengan koordinat Lintang 1°57'35.16442"N Bujur 100°0'35.09878"E dan (CTJB) Tanjung Balai dengan koordinat Lintang 1°44'27.42027" N Bujur 99°48'35.13624" E dengan menggunakan Metode Statik Pengolahan Post Processing.

LEGENDA

BATAS ADMINISTRASI :
- Batas Desa
- Batas Kecamatan
- Batas Kabupaten
- Batas Propinsi
- Batas Negara

BATAS FISIK DAN BANGUNAN :
- Batas Bidang Tanah
- Bangunan
- Bangunan Bertingkat
- 18345 Nomor Bidang Tanah

PERAIRAN DAN VEGETASI :
- Sungai / anak sungai
- Saluran Irigasi Teknis
- Saluran air / got
- Danau
- Rawa
- Belukar, Hutan, Pinus
- Jati, Karet, Kina
- Cokiat, Lada, Cengkeh
- Kelapa, Sawit, Sagu
- Tembakau, Tebu, Teh

JALAN, REL, K.A DAN JEMBATAN
- Jalan Aspal
- Jalan Tanah
- Rel Kereta Api
- Rel Lori
- Jembatan

TITIK / TANDA BATAS :
- Tugu Beton
- Tugu Besi
- Tugu Paralon
- Kayu Besi (sejenis)
- Besi Siku/Pipa
- Base

Batas-batas pada Peta Bidang Tanah ini merupakan batas tanah yang dimohon dan ditunjuk oleh pemohon yang dapat diverifikasi atau diinformasikan apabila didalamnya terdapat penguasaan/pemilikan oleh pihak lain atau termasuk areal yang terlarang (restricted area) yang diatur dalam peraturan perundangan yang berlaku, Berdasarkan Peraturan Menteri Agraria dan Tata Ruang/Kepala Badan Pertanahan Nasional Nomor 18 Tahun 2021 Bidang Tanah ini belum sepenuhnya tidak terdapat persoalan Hak bidang tanah.

Peta Bidang Tanah ini bukan merupakan bukti kepemilikan hak atas tanah

BADAN PERTANAHAN NASIONAL
KANTOR WILAYAH PROVINSI SUMATERA UTARA
BIDANG SURVEI DAN PEMETAAN

PEMETAAN KELILING BATAS TANAH
PT. PERKEBUNAN NUSANTARA IV

P E M E T A A N		Paraf/Tanggal
No. Berkas	235/2023	–
Prosedur	Pengukuran dan Pemetaan Kadastral	–
Nama Pemohon	Suripto Prayitno	–
Alamat	Jl. Letjend Suprapto No.2 Medan	–
No. D.I. 302	41/2023 Tanggal 02/11/2023	–
No. GU	58/2023 Tanggal 20/11/2023	–
Luas	Lihat Keterangan	–
Diukur dan digambar oleh	Evan Berta Pramudhita, S.T.	
	Yudo Pangestu	04-03-24
	Aryo Riza Yudhanto	06-03-24
	Annisa Astrini	
	Lestari Agustin	04-03-24
Koordinator	Ahmad Risdi Tanjung, S.P, M.Si.	06-03-24
Diperiksa oleh	Abdul Rahman Irianto, S.ST.	06-03-24

Medan, 06 Maret 2024
Untuk Pembuatan,
Kepala Bidang
Survei dan Pemetaan

Dessy Lukmansyah, S.T.
NIP. 19870921 199703 1 001